
ENMORE THEATRE
DMX NODE GATEWAY UPGRADE

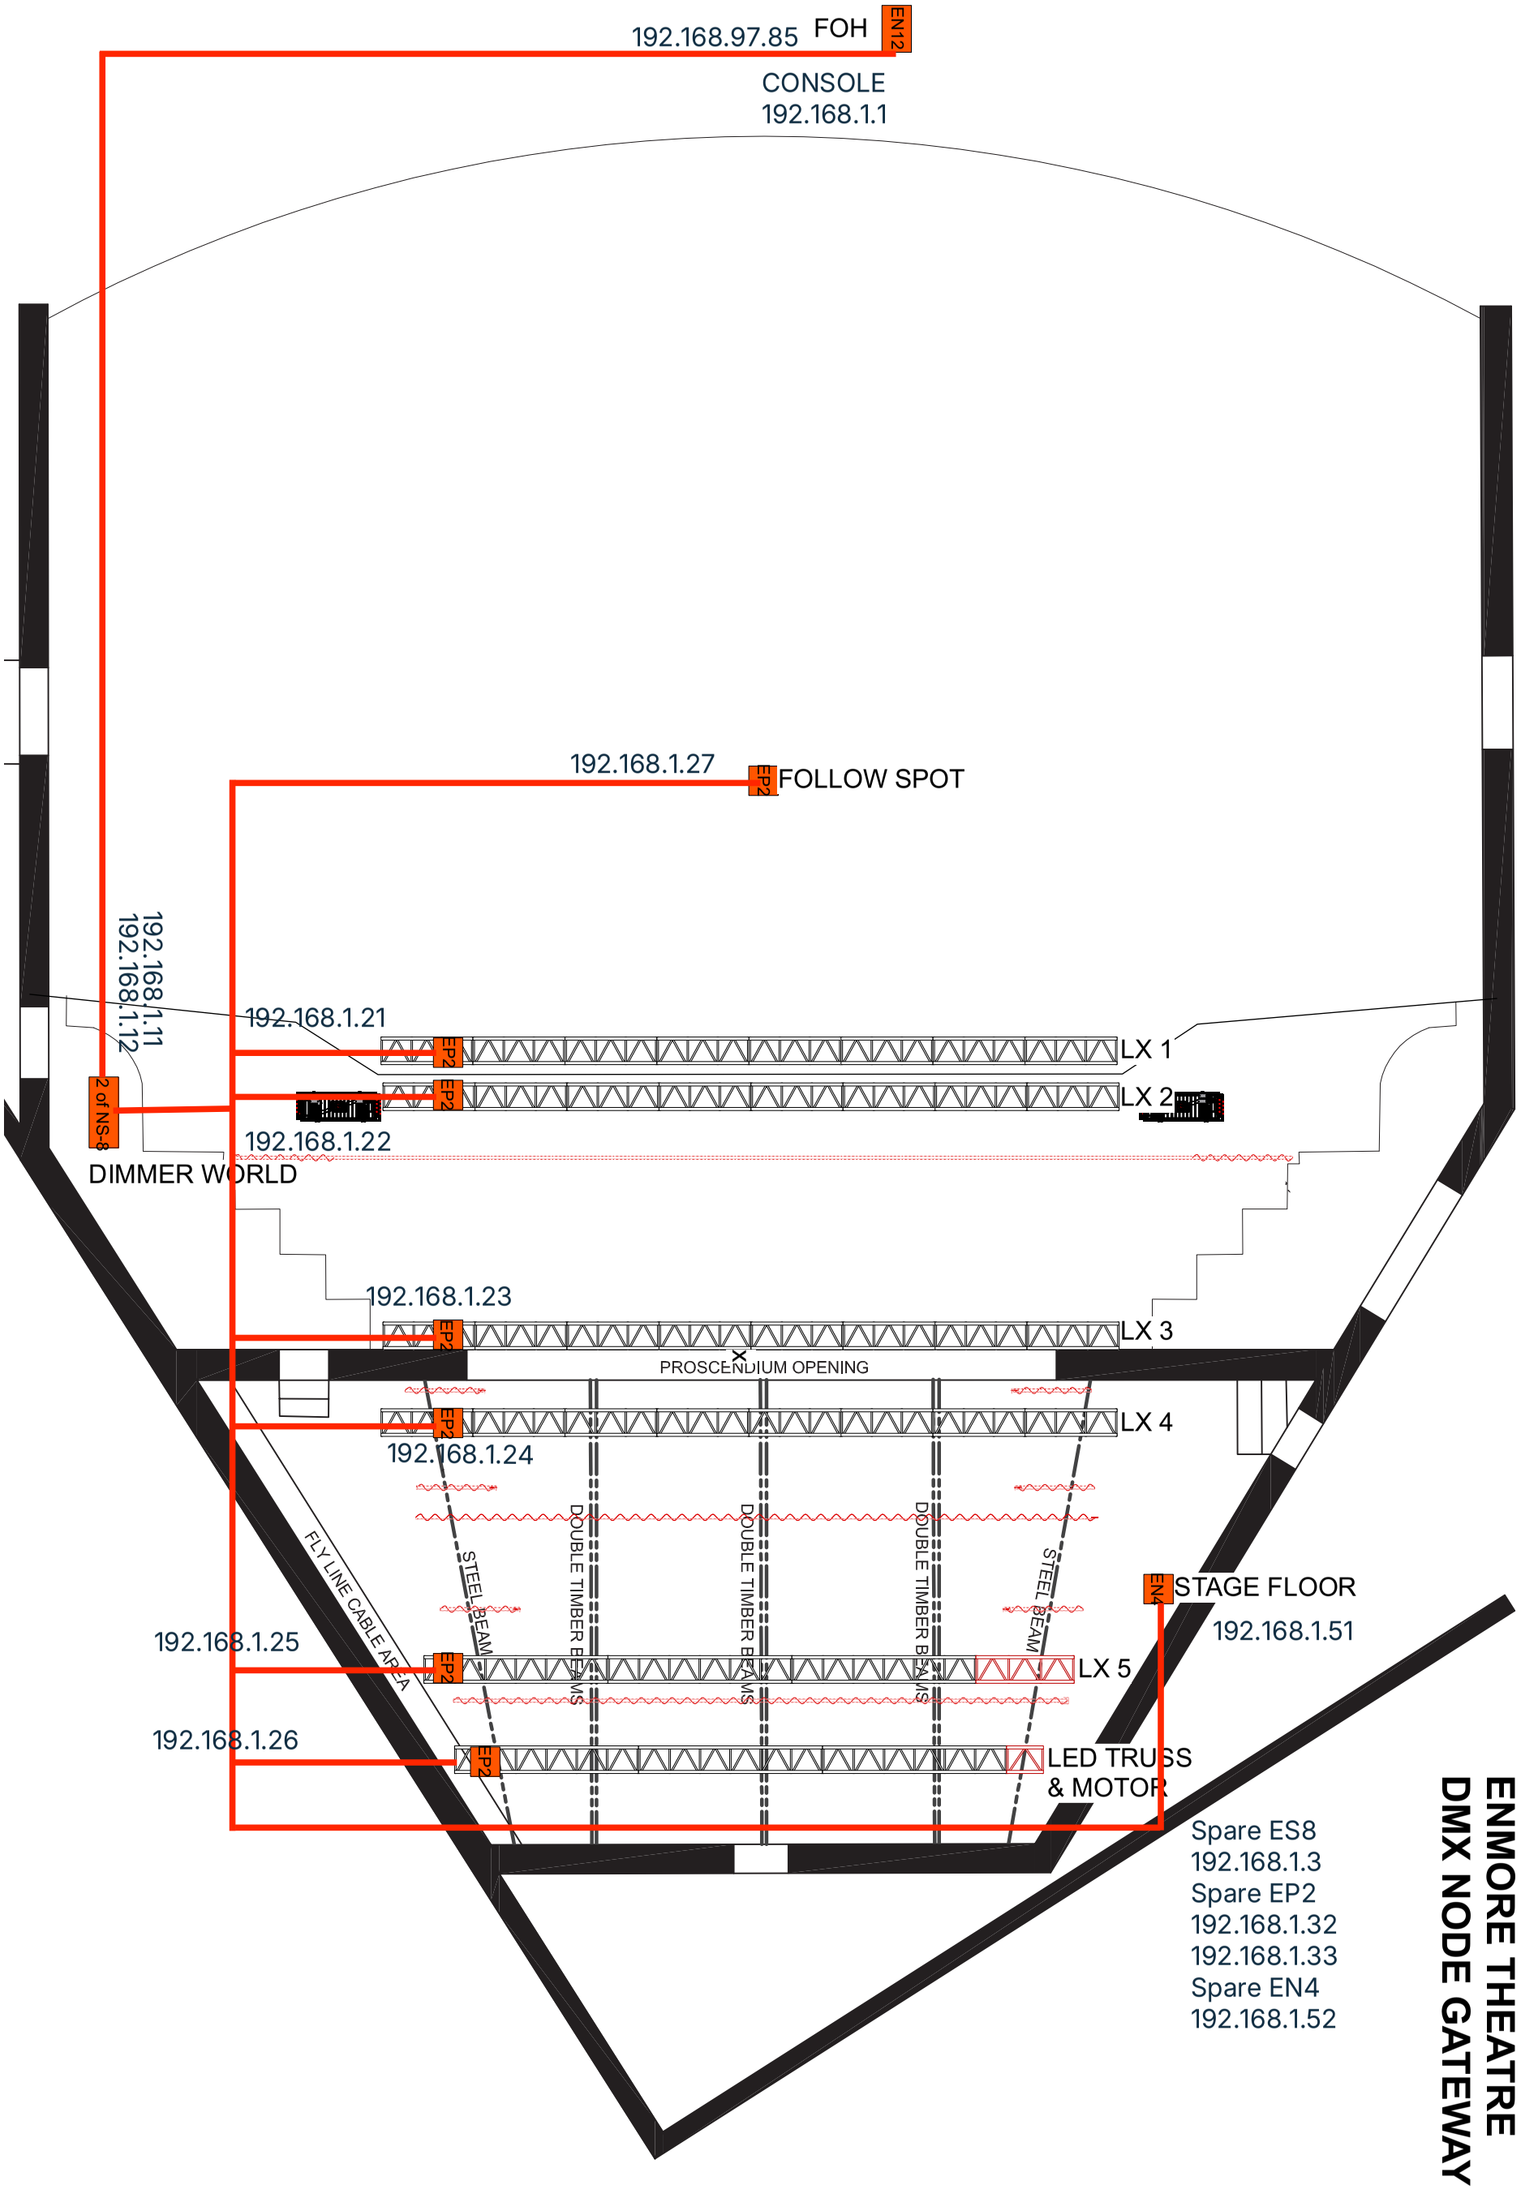

Spare ES8
192.168.1.3
Spare EP2
192.168.1.32
192.168.1.33
Spare EN4
192.168.1.52

Scale 1:100