



Page 01: Plot

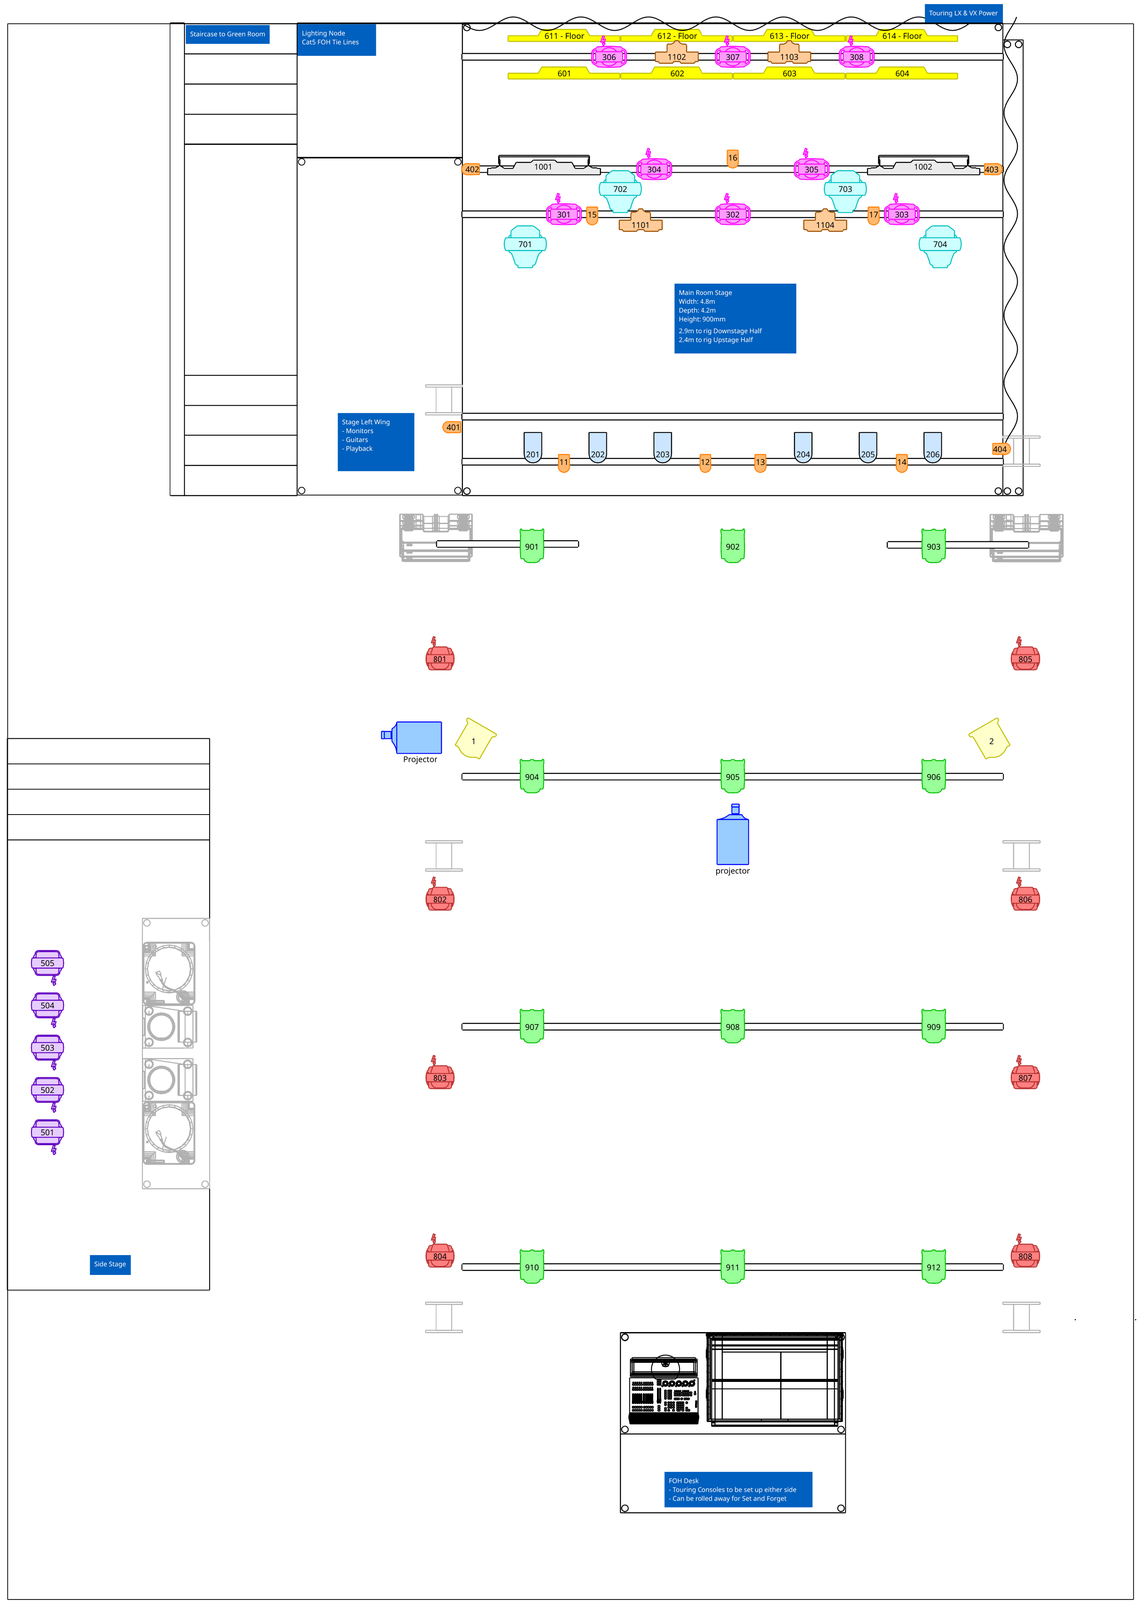

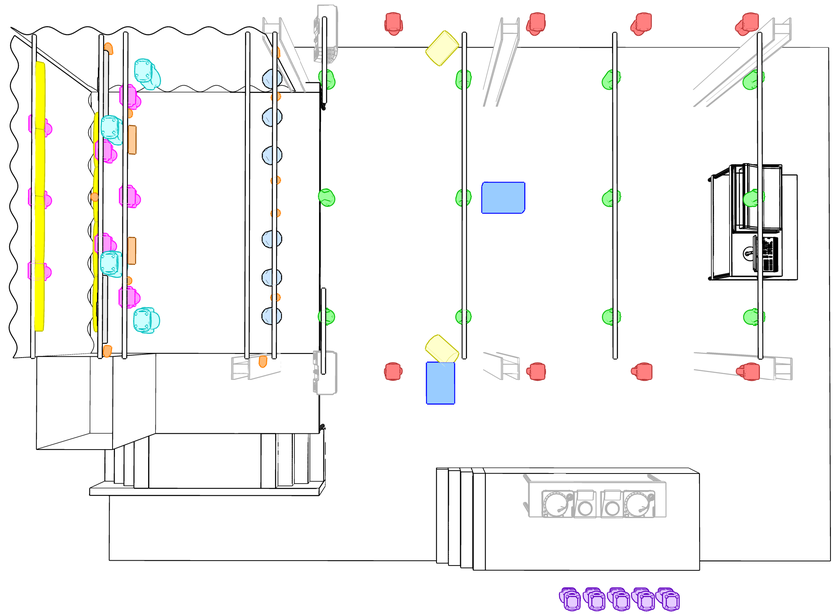

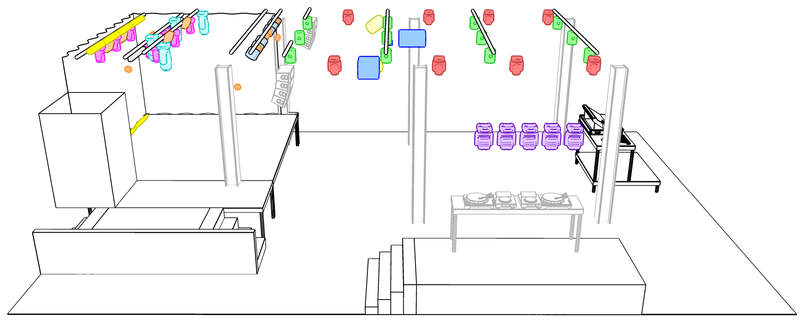

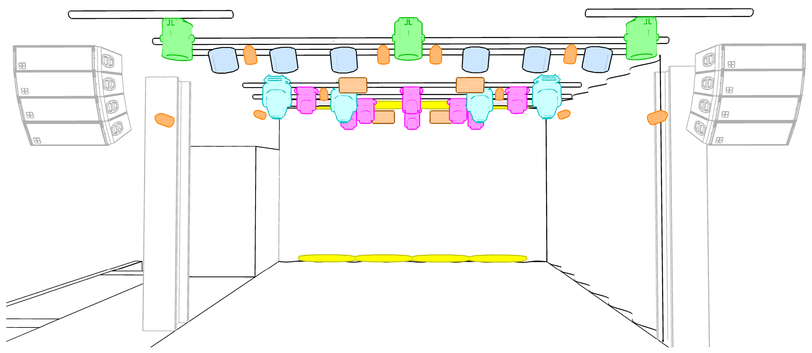

Scale: 1:27.22

Project

Main Room - Standard Rig

Project Location
OAF Main Room

Current as of
September 2025

Drawn By
Jackson Stocks

Lighting Designer
Jackson Stocks

Contact
E: lighting@oxfordartfactory.com
M: +61 431 779 917

Fixture Symbol Key

Stage
- 8x Mini B - 21ch
- 4x Era 300 Spot - 21ch
- 8x FusionBar Q VX - 53ch
- 2x Tambora Linear 100 - 139ch
- 4x Blinder ii C - 29ch
- 11x Par 16 Birdie - 1ch
- 2x WW LED Fresnel - 5ch
- 6x Pro Shop LED Par - 10ch

Dancefloor & Side Stage
- 8x Pixie Wash - 16ch
- 12x Jet Par 7ZIP - 20ch
- 5x Beamz 22 - 25ch

Video
- Video Projector (2)

Control
[2.0.0.1] GrandMA3 OnPC Command Wing
[2.0.0.11] Luminex Luminode 12

Atmosphperics
1x Unique 2.1

Staging & Rigging

- 4.8m Wide
- 4.2m Deep

- 2.9m Deck to LX Bar [Downstage Half]
- 2.4m Deck to LX Bar [Upstage Half]

- 5x 4.8m Wide LX Bars [Stage]
- 3x 4.8m Wide LX Bars [Dance Floor]

OAF Main Room has a sufficient lighting package, suitable for all requirements and needs. Thus, OAF does not allow for additions to be rigged to the venue infrastructure, and no plot adjustments are to be made.

Drawing Date
04/12/2025

Version
1.0

Revision Date
XX/XX/XXXX

Paper Print Size
A1 Horiztontal

File Name
OAF_StandardRig_2512

The Design and all associated paperwork is copyrighted and remains the property of the designer

The design is for one time use only at the specified location and is not to be used for any other purpose or event without specific permission of the designer

The Designer is not a structural engineer and these drawings represent design concepts only and are not intended as engineering drawings. The designer assumes no responsibility for the safety or structural integrity of any equipment provided by anyone

© Jackson Stocks, 2025. All RIghts Reserved